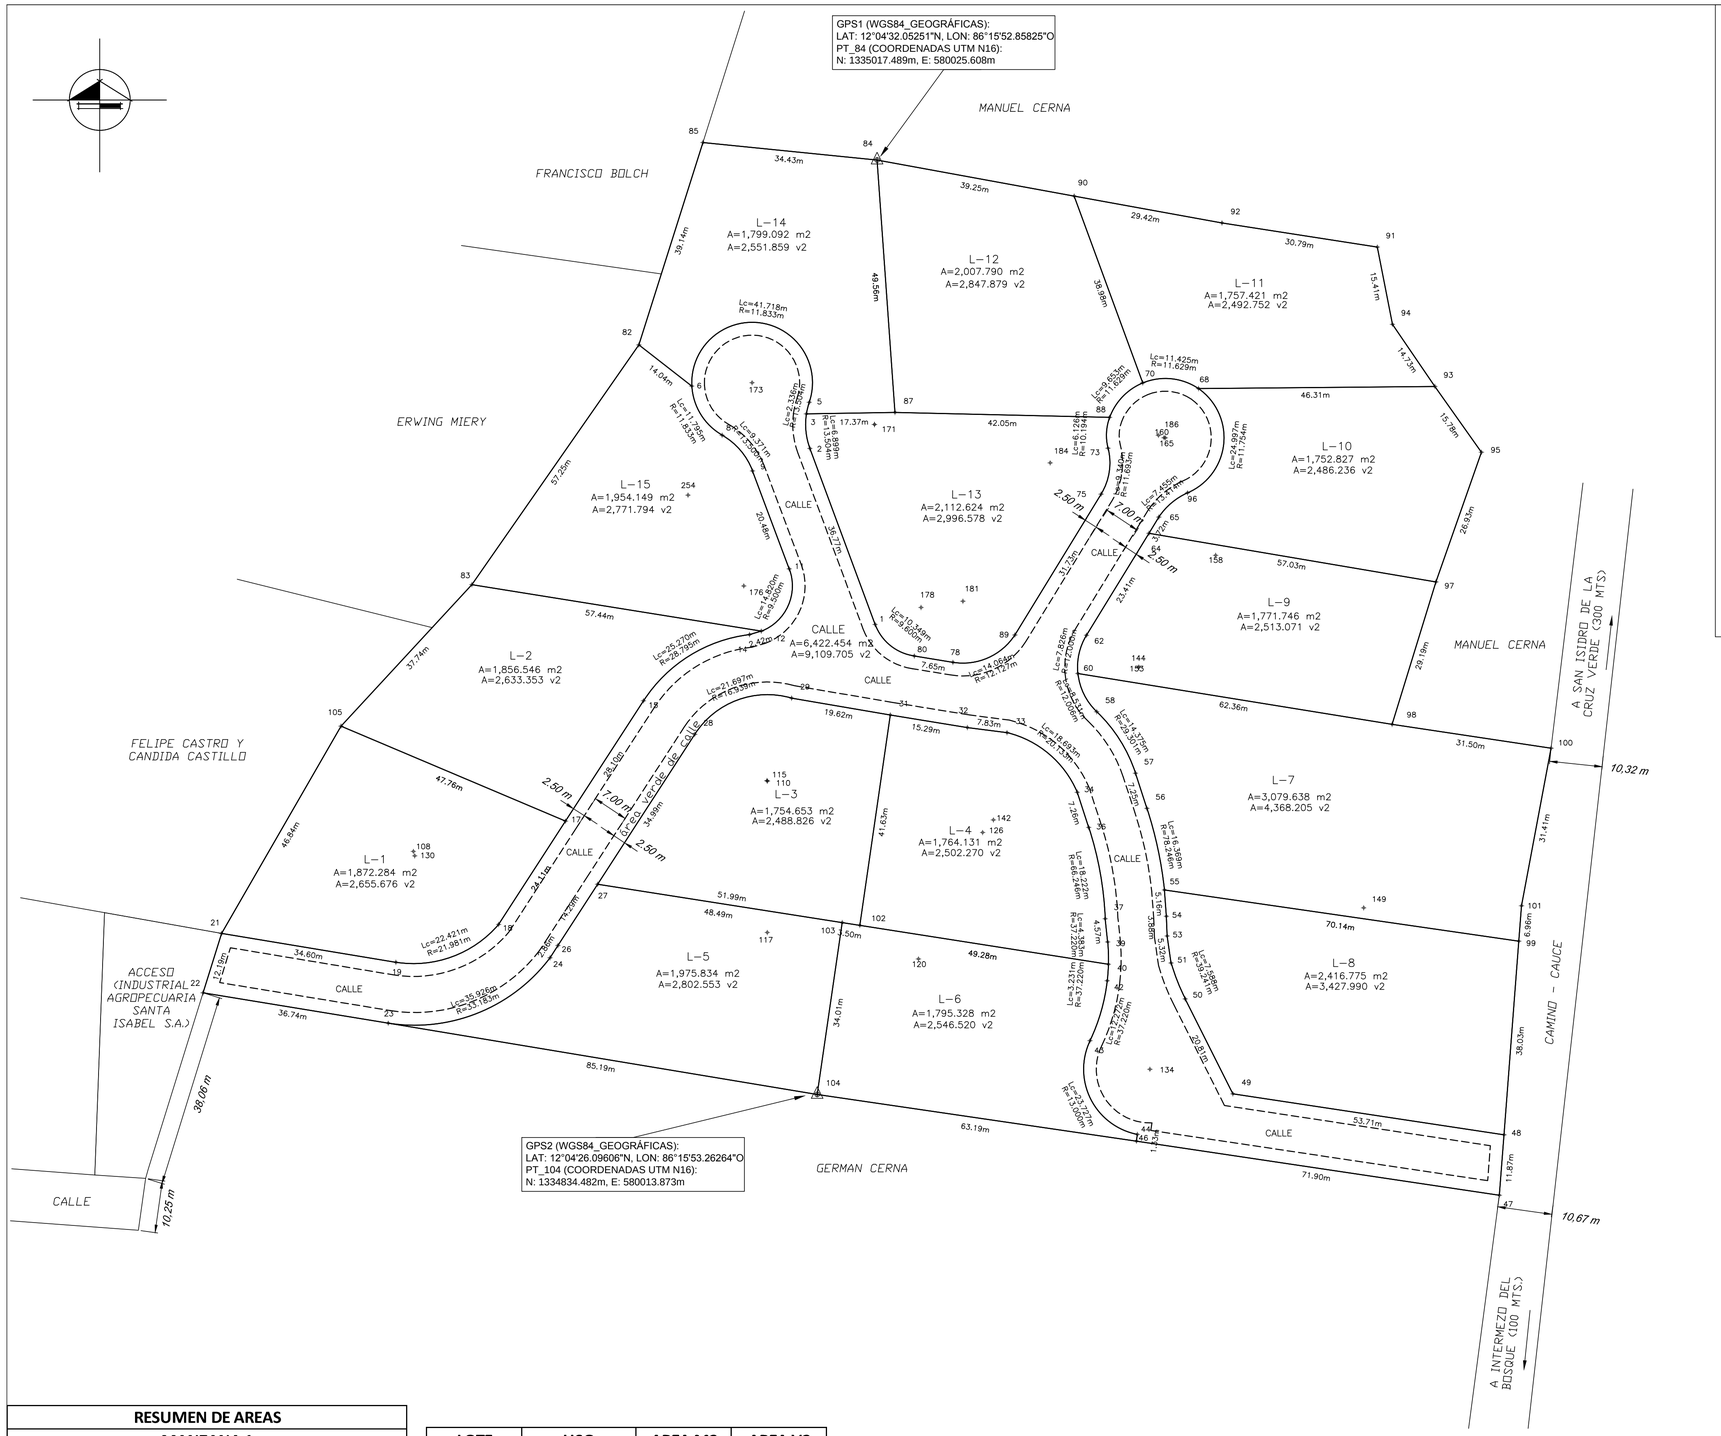

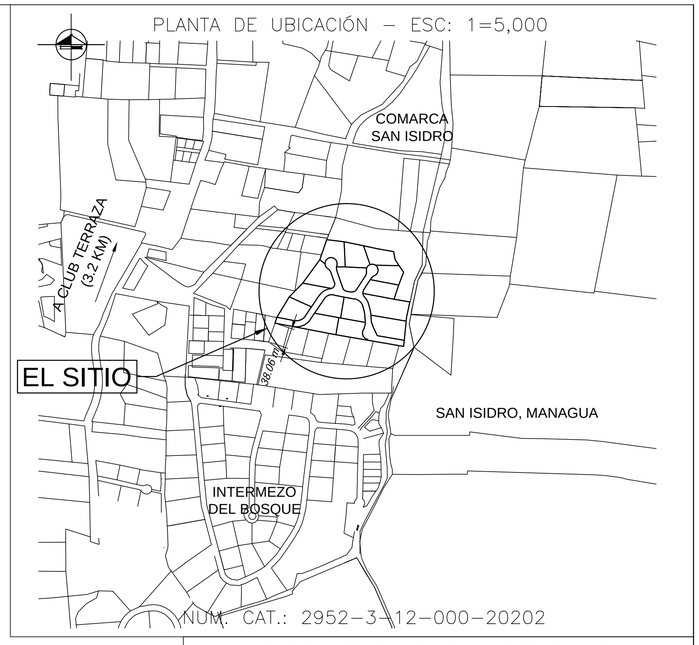

MEMORIA DE CALCULO – LOTE GENERAL

LADO EST	LADO PV	RUMBO	DISTANCIA	V	COORDENADAS Y	COORDENADAS X
				21	1,334,866.0336	579,897.1972
21	105	N 29°57'17.65" E	46.840	105	1,334,906.6164	579,920.5852
105	83	N 42°46'27.34" E	37.738	83	1,334,934.3176	579,946.2137
83	82	N 34°52'15.48" E	57.247	82	1,334,981.2851	579,978.9432
82	85	N 17°34'04.16" E	41.570	85	1,335,020.9164	579,991.4906
85	84	S 84°15'46.19" E	34.289	84	1,335,017.4887	580,025.6076
84	90	S 79°38'10.57" E	39.245	90	1,335,010.4287	580,064.2123
90	92	S 79°42'00.43" E	29.424	92	1,335,005.1677	580,093.1621
92	91	S 81°09'18.41" E	30.794	91	1,335,000.4329	580,123.5894
91	94	S 11°08'13.85" E	15.413	94	1,334,985.3102	580,126.5666
94	93	S 34°20'28.88" E	14.732	93	1,334,973.1457	580,134.8775
93	95	S 35°17'46.60" E	15.784	95	1,334,960.2628	580,143.9979
95	97	S 19°20'06.11" W	26.928	97	1,334,934.8539	580,135.0823
97	98	S 17°06'55.53" W	29.185	98	1,334,906.9610	580,126.4931
98	100	S 81°29'11.42" E	31.498	100	1,334,902.2979	580,157.6439
100	101	S 10°38'02.36" W	31.409	101	1,334,871.4288	580,151.8480
101	99	S 04°22'34.12" W	6.962	99	1,334,864.4866	580,151.3167
99	48	S 04°22'34.12" W	38.031	48	1,334,826.5665	580,148.4148
48	47	S 04°22'34.12" W	11.871	47	1,334,814.7300	580,147.5090
47	46	N 81°31'03.07" W	71.901	46	1,334,825.3359	580,076.3947
46	104	N 81°40'38.81" W	63.187	104	1,334,834.4819	580,013.8732
104	23	N 80°34'19.55" W	85.193	23	1,334,848.4371	579,929.8311
23	22	N 80°40'35.68" W	36.743	22	1,334,854.3896	579,893.5739
22	21	N 17°17'06.44" E	12.195	21	1,334,866.0336	579,897.1972

AREA = 36,093.292 m2 = 51,195.267 v2 =
3 Ha + 6,093.292 m2 = 5 Mz + 1,195.267 v2

RESUMEN DE AREAS

MANZANA 1

LOTE	USO	AREA M2	AREA V2
1	Habitacional	1,872.284	2,655.676
2	Habitacional	1,856.546	2,633.353
3	Habitacional	1,754.653	2,488.826
4	Habitacional	1,764.131	2,502.270
5	Habitacional	1,975.834	2,802.553
6	Habitacional	1,795.328	2,546.520
7	Habitacional	3,079.638	4,368.205
8	Habitacional	2,416.775	3,427.990
9	Habitacional	1,771.746	2,513.071
10	Habitacional	1,752.827	2,486.236
11	Habitacional	1,757.421	2,492.752
12	Habitacional	2,007.790	2,847.879
13	Habitacional	2,112.624	2,996.578
14	Habitacional	1,799.092	2,551.859
15	Habitacional	1,954.149	2,771.794

USO	AREA M2	AREA V2
Calle	6,422.454	9,109.705

TOTALES

USO	AREA M2	AREA V2
Habitacional	29,670.838	42,085.562
Calle	6,422.454	9,109.705
TOTAL:	**36,093.292**	**51,195.267**

Objeto :	PLANO MOSAICO "LOTIFICACIÓN SANTA ISABEL"	Ubic.:	SANTA ISABEL, COMARCA DE SAN ISIDRO DE LA CRUZ VERDE, MANAGUA
Propietario :	INDUSTRIAL AGROPECUARIA SANTA ISABEL S.A.		
Area :	36,093.292 m2 = 51,195.267 v2	Ejecutó :	JOSÉ MANUEL LÓPEZ PRADO
	3 Ha + 6,093.292 m2 = 5 Mz + 1,195.267 v2	Lic. Cat.:	JML010069 — Firma:
Escala :	1 : 600 — No. Plano: 1 / 2	Fecha :	01 DE FEBRERO DE 2017